
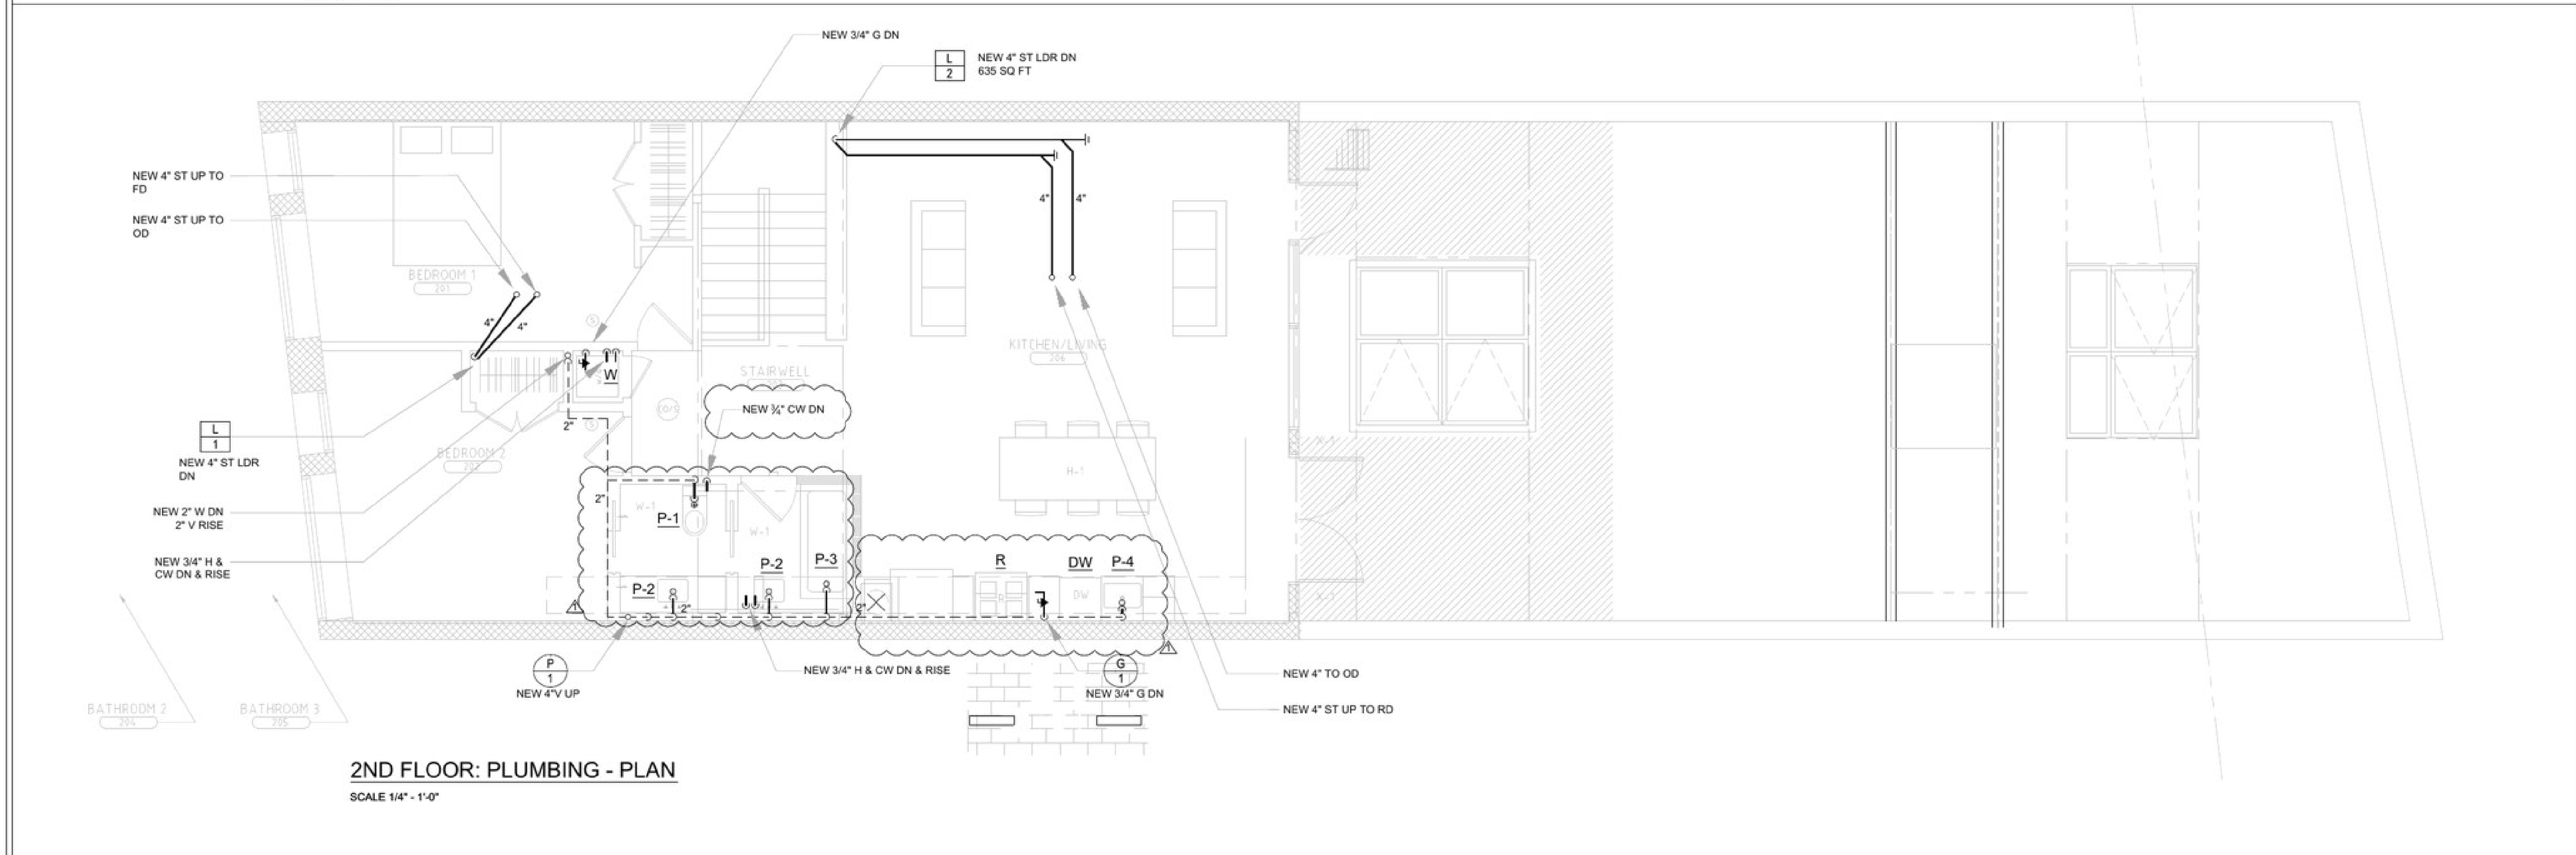


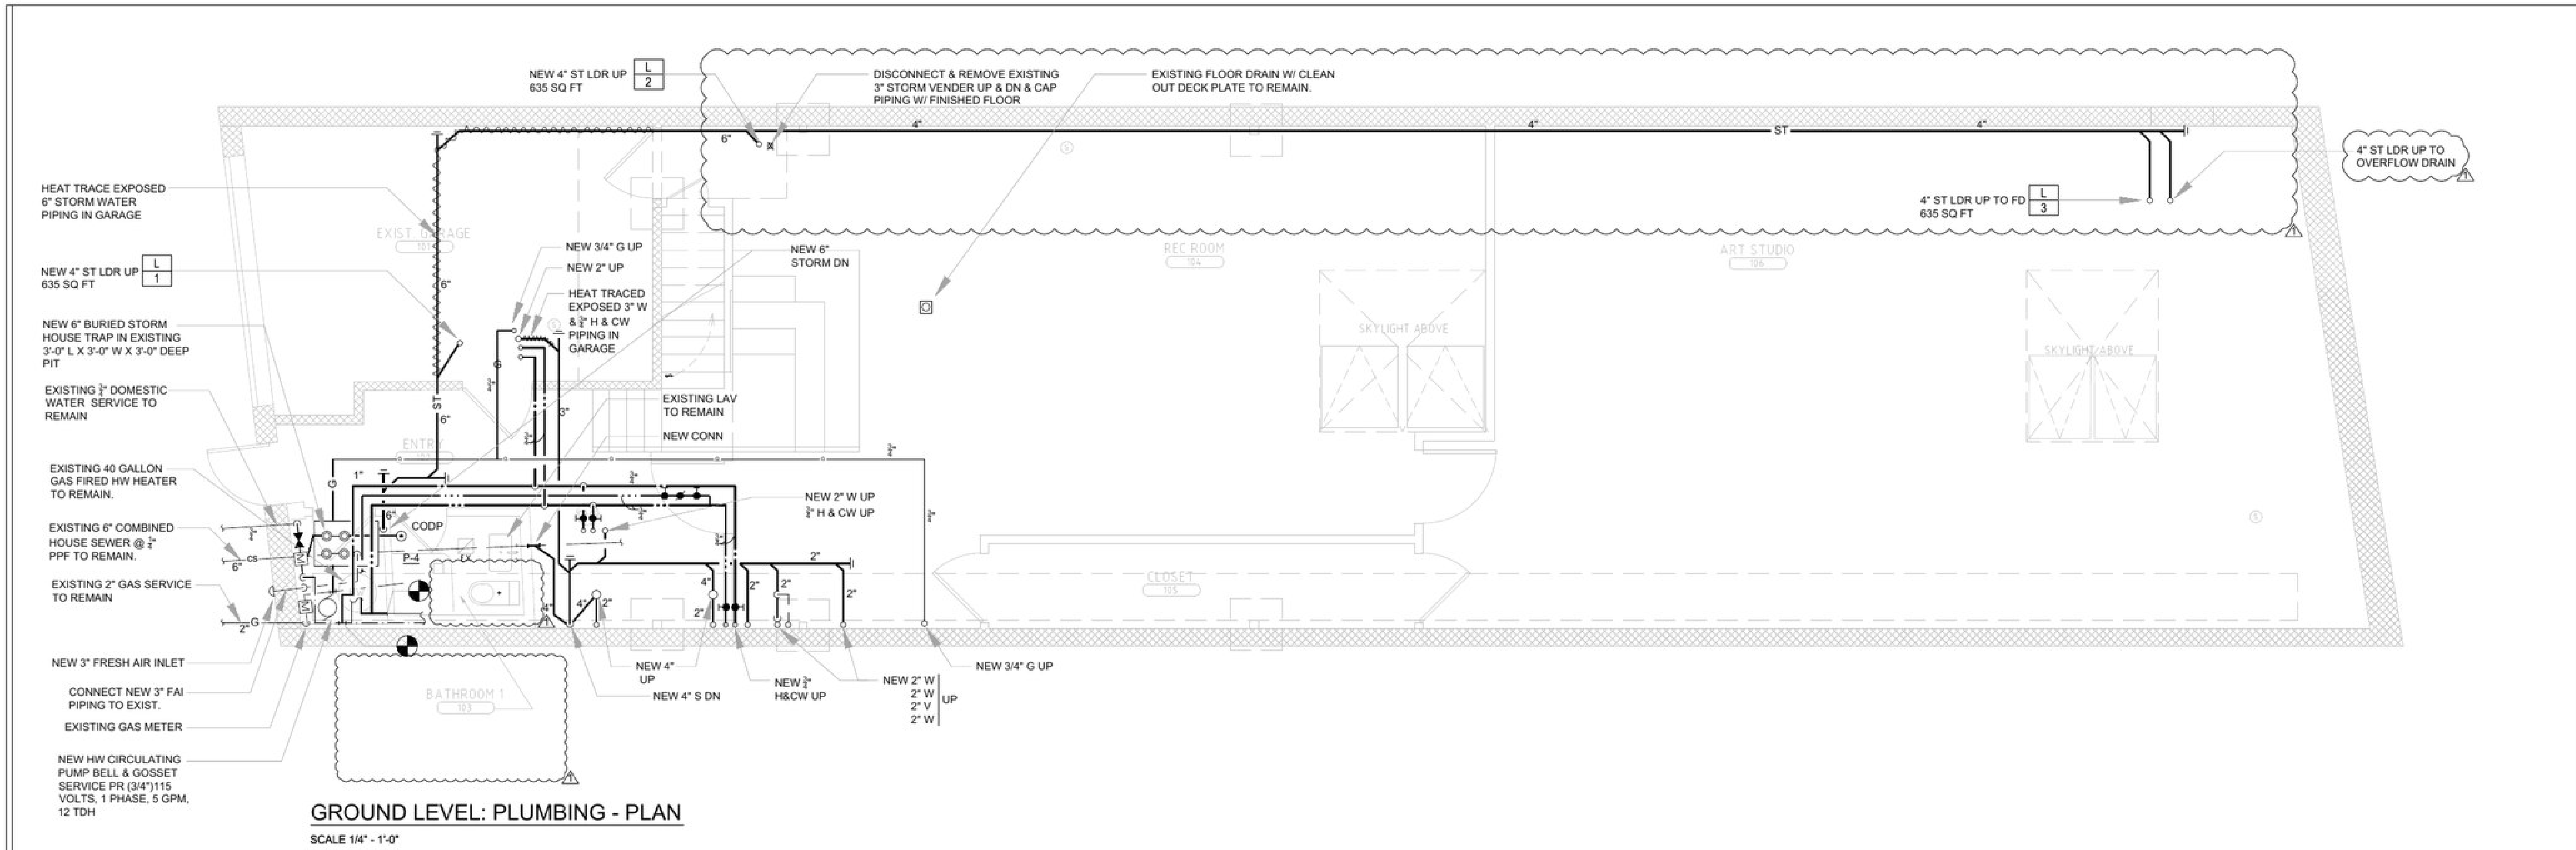

S s D

325 W 38TH STREET, SUITE 210
NEW YORK, NY 10018

tel: 212.248.7500
fax: 866.677.3878
www.ssdarchitecture.com
info@ssdarchitecture.com

CONSULTANTS:

MECHANICAL ELECTRICAL PLUMBING CONSULTANT:

TWIG
Consulting Engineers, PC

7 Penn Plaza - Suite 702, New York, NY 10001
Tel: 212.967.7700 / Fax: 212.967.8948
info@twig.com www.twig.com

STRUCTURAL ENGINEER:

Richard H. Balser, Engineers
228 W 18th Street, No. 11
New York, NY 10011
T 212-463-0008

SURVEYOR:

Leonard J. Strandberg and Associates
Consulting Engineers and
Land Surveyors, P.C.
92 Atlantic Avenue, Freeport, NY 11520
516-378-2064 212-213-4090
fax 516-378-6649

07/03/2012 ISSUED FOR CONSTRUCTION

PROJECT:

HSU HOUSE

PROJECT ADDRESS:

94 NORTH FIRST STREET
BROOKLYN, NY 11211

DWG TITLE:

**GROUND & 2ND LEVEL
PLUMBING
PLAN**

SEAL & SIGNATURE:

DATE: 23 NOV 2011

PROJECT NO.:

DWG BY: CAD

CHK BY: TWG

DWG NO.:

P-301.00

DWG IS NO.:

PAGE NO.:

3 of 3

NYC ECC EXEMPTION:
THE PLUMBING APPLICATION IS EXEMPT FROM
THE NYC ENERGY CONSERVATION CODE (NYC
ECC) AS PER SECTION 101.6

THESE PLANS ARE APPROVED ONLY FOR THE WORK ON THE
APPLICATION SPECIFICATION SHEET. ALL OTHER MATTERS SHOWN
ARE NOT TO BE RELIED UPON OR TO BE CONSIDERED AS EITHER
BEING APPROVED OR IN ACCORDANCE WITH APPLICABLE CODES.

ADDED CALIBRATION GUIDE: 10 ft

Derived from source 1/4 inch = 1 foot at 36 x 24 inch sheet size. Verify before use.